




GERAL

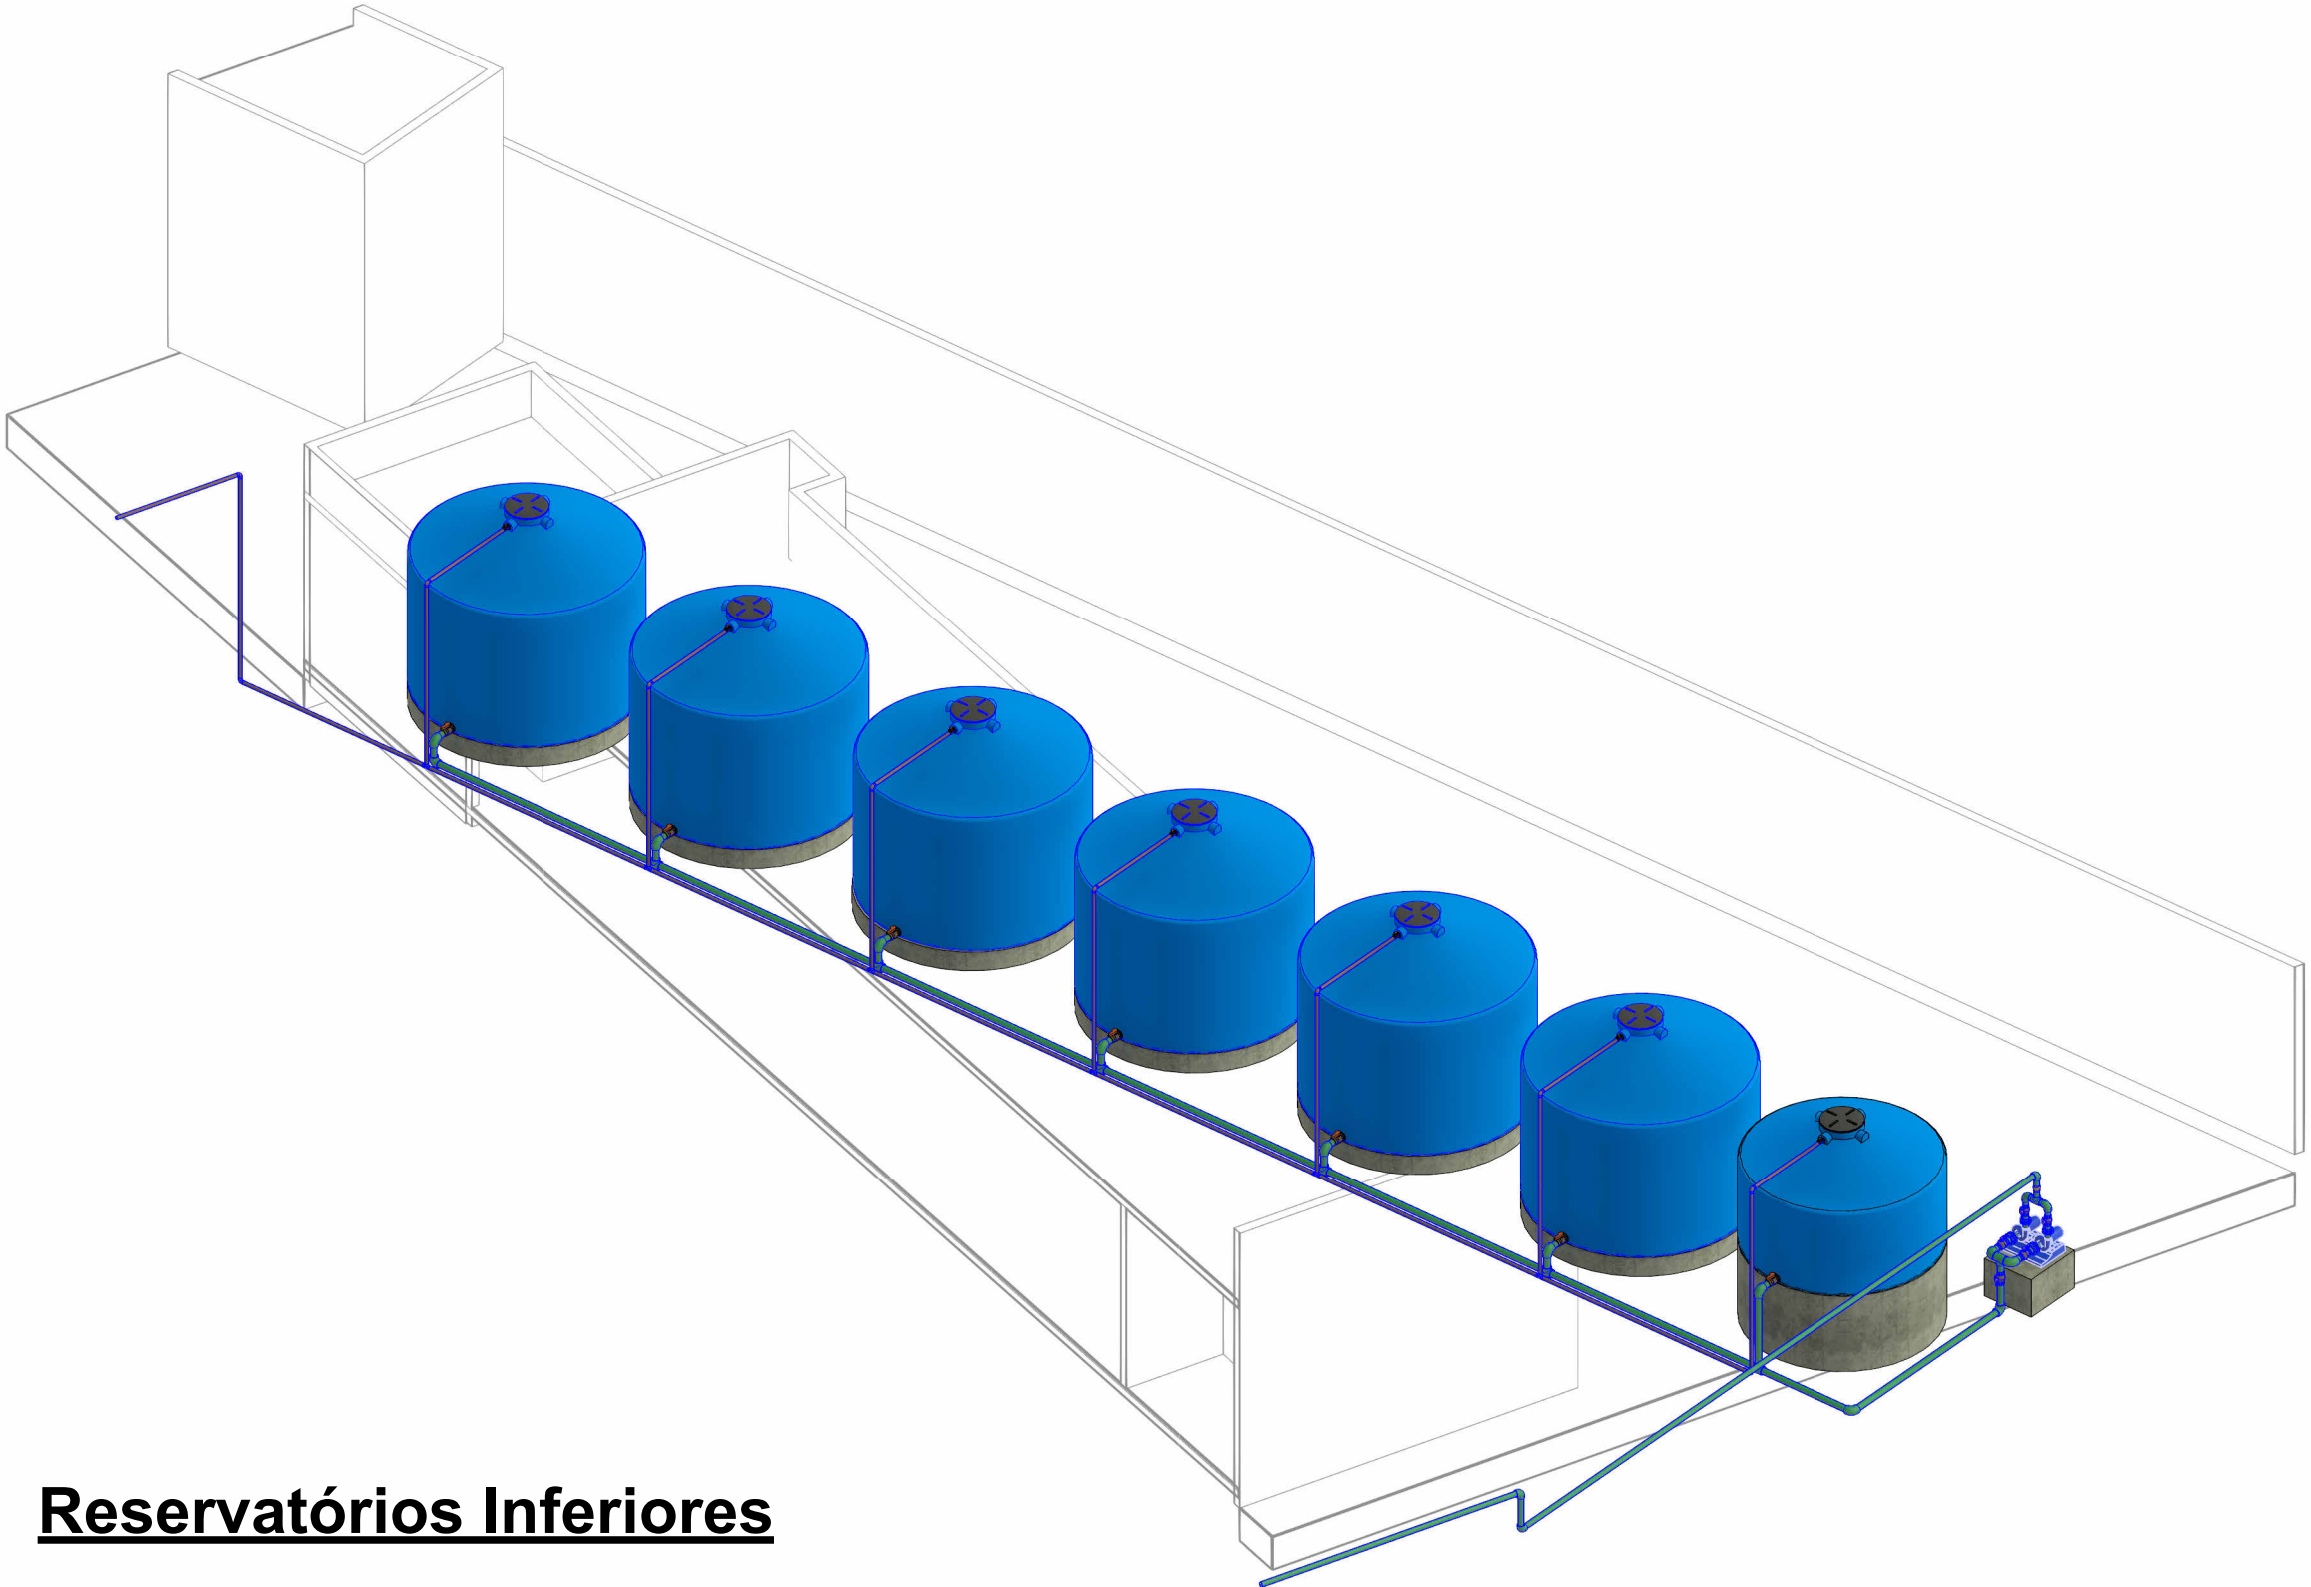

Reservatórios Inferiores

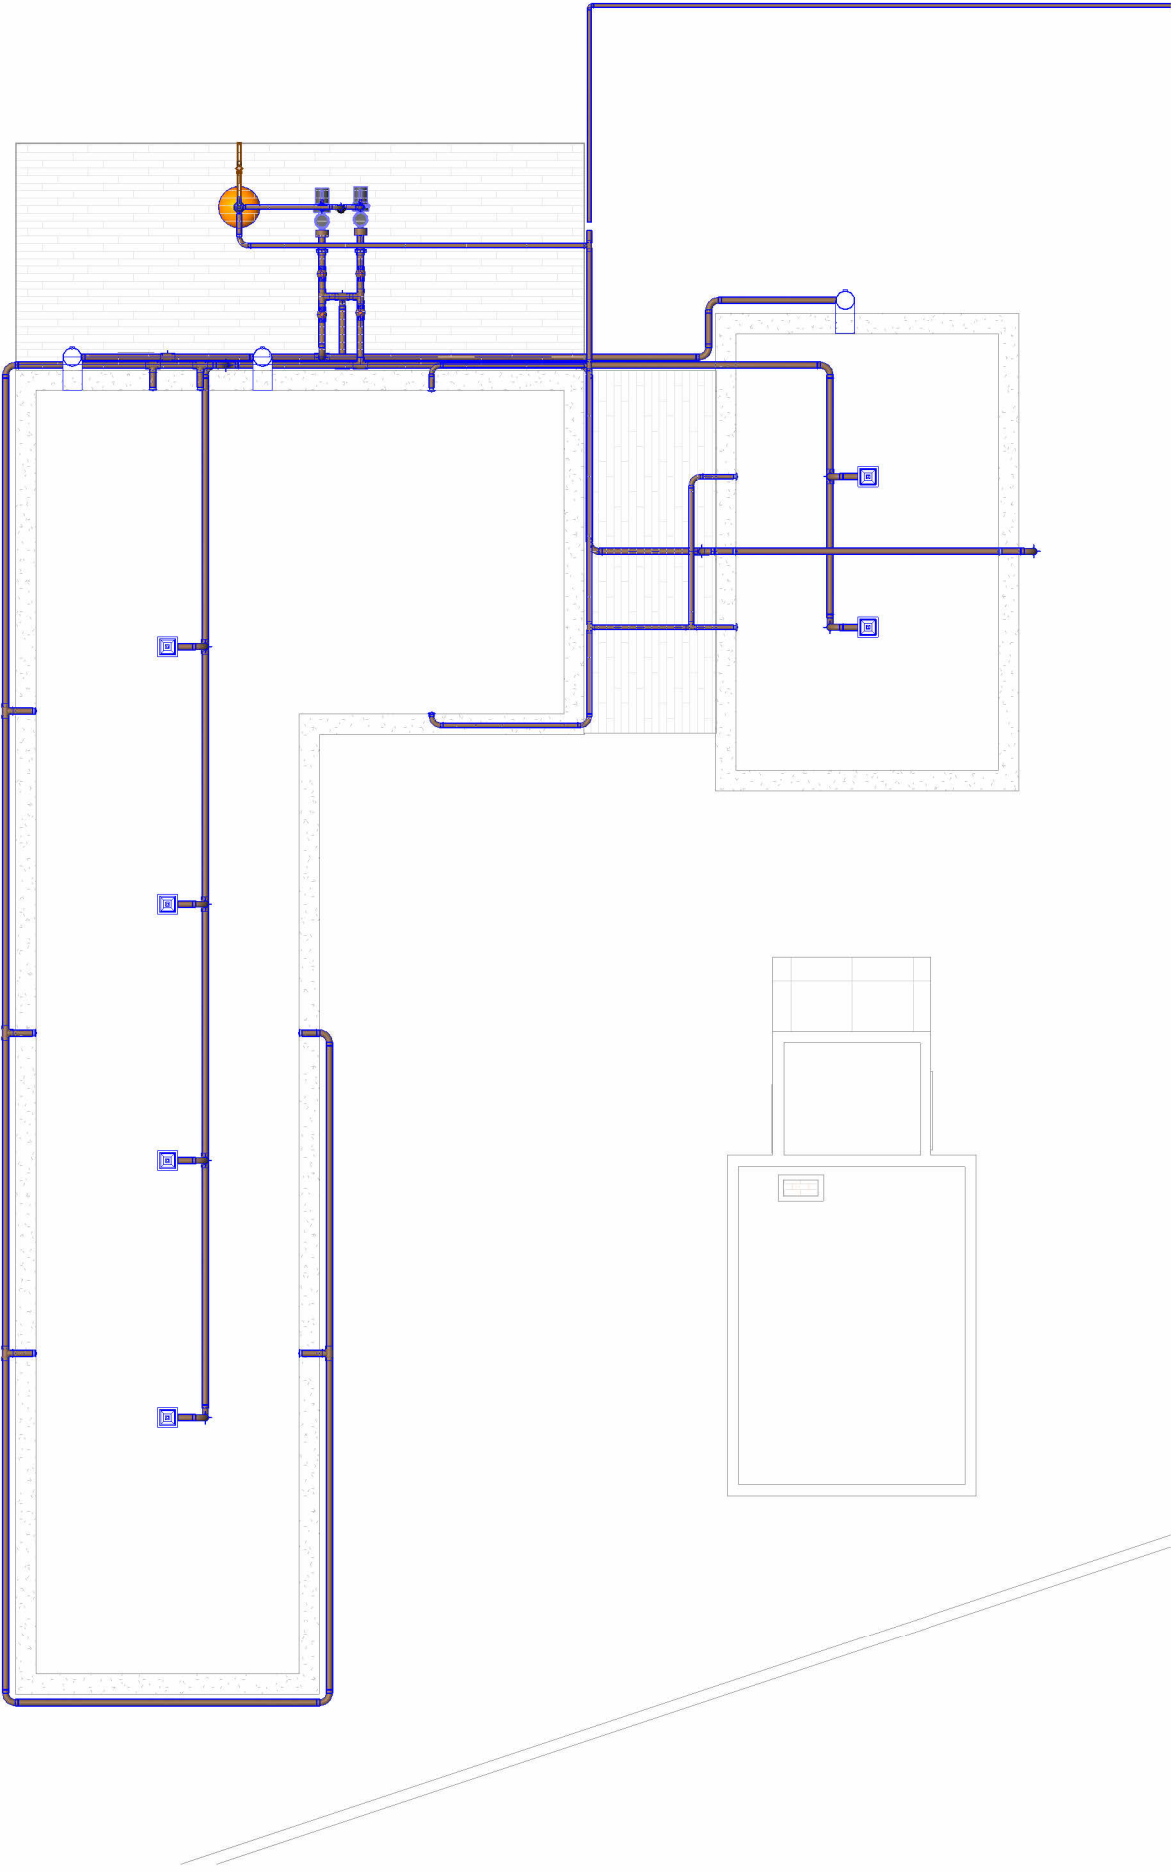

Planta Baixa Piscina
1 : 100

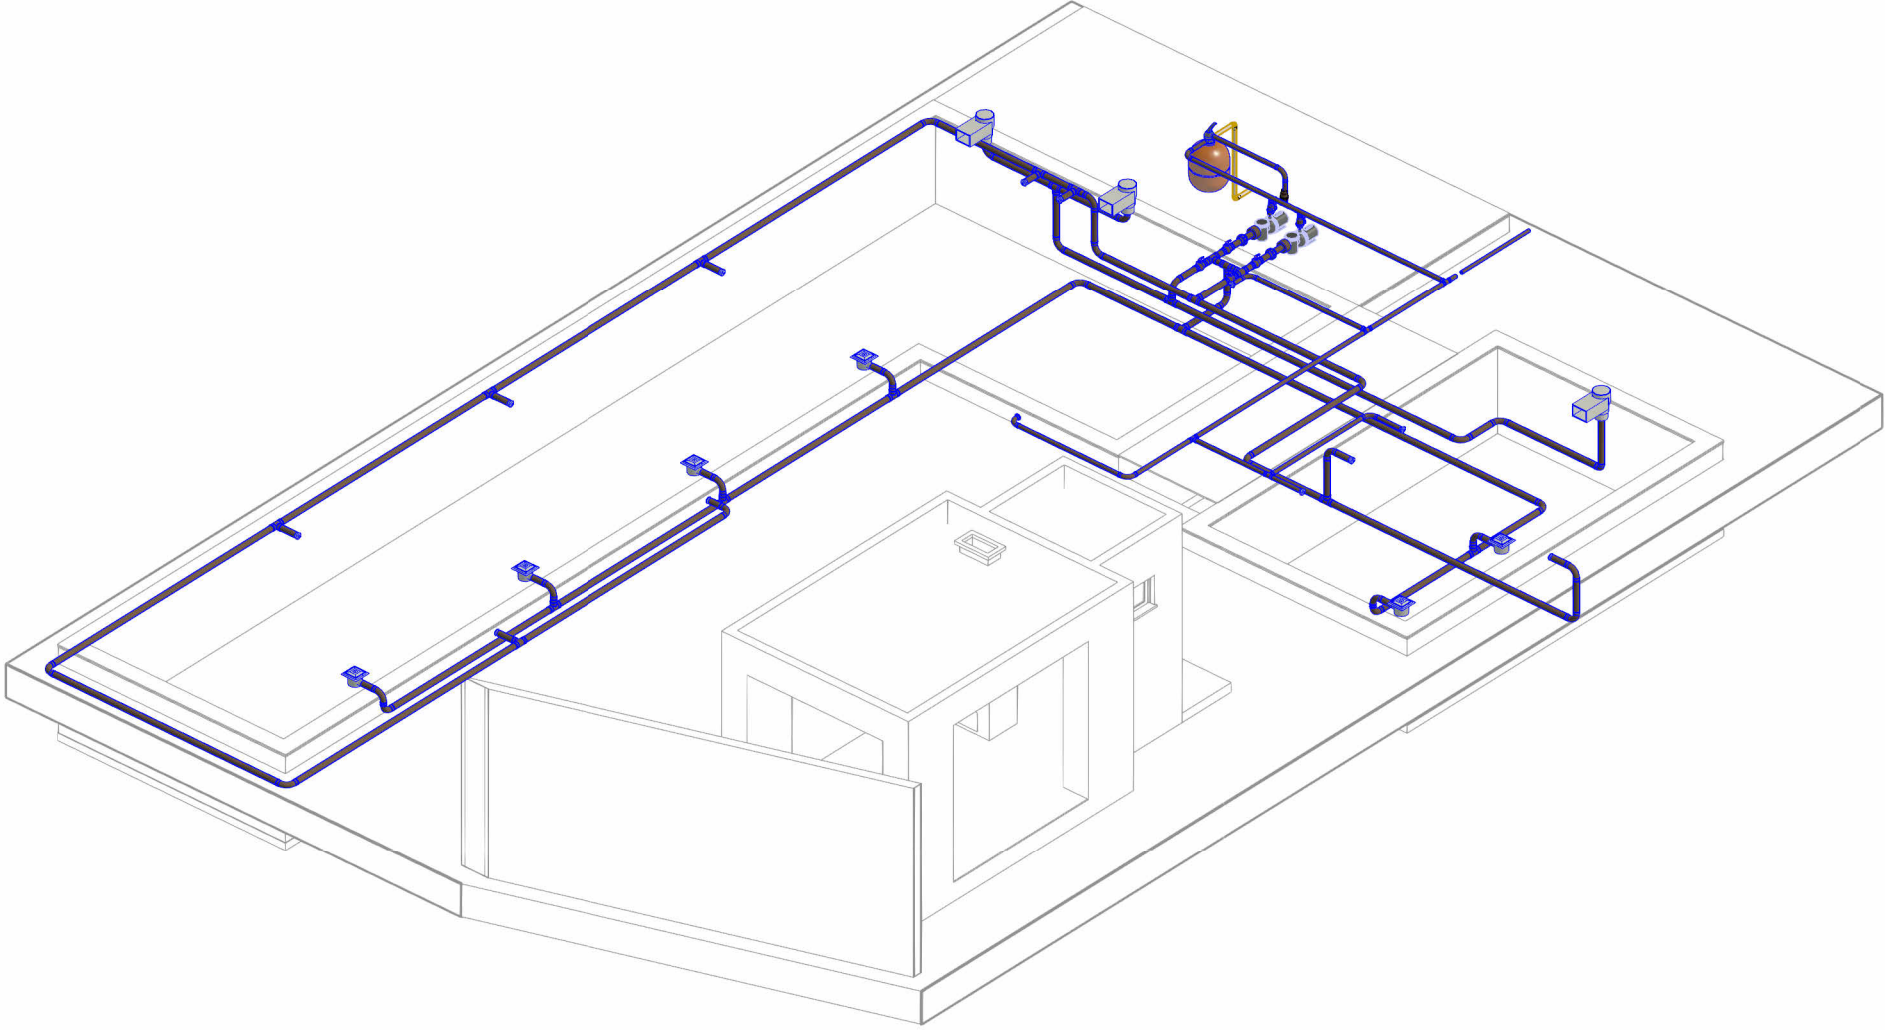

Isométrico Piscina



PENN & WIZE
INSTALAÇÕES PREDIAIS
<https://pennwize.github.io/>

PROJETO:	EDIFÍCIO DERRY AND GEORGIE	FOLHA:	01
LOCAL:	Rua dos bobos, nº 0	REV.:	
ASSUNTO:	INSTALAÇÕES HIDROSSANITÁRIAS - ÁGUA QUENTE E FRIA	ESCALA:	1 : 100
AUTORES DO PROJETO:	AMANDA C, JOÃO PEDRO M, LETÍCIA T	DATA:	23/01/26



2° Pavimento
1 : 50



PENN & WIZE
INSTALAÇÕES PREDIAIS
<https://pennwize.github.io/>