



GERAL

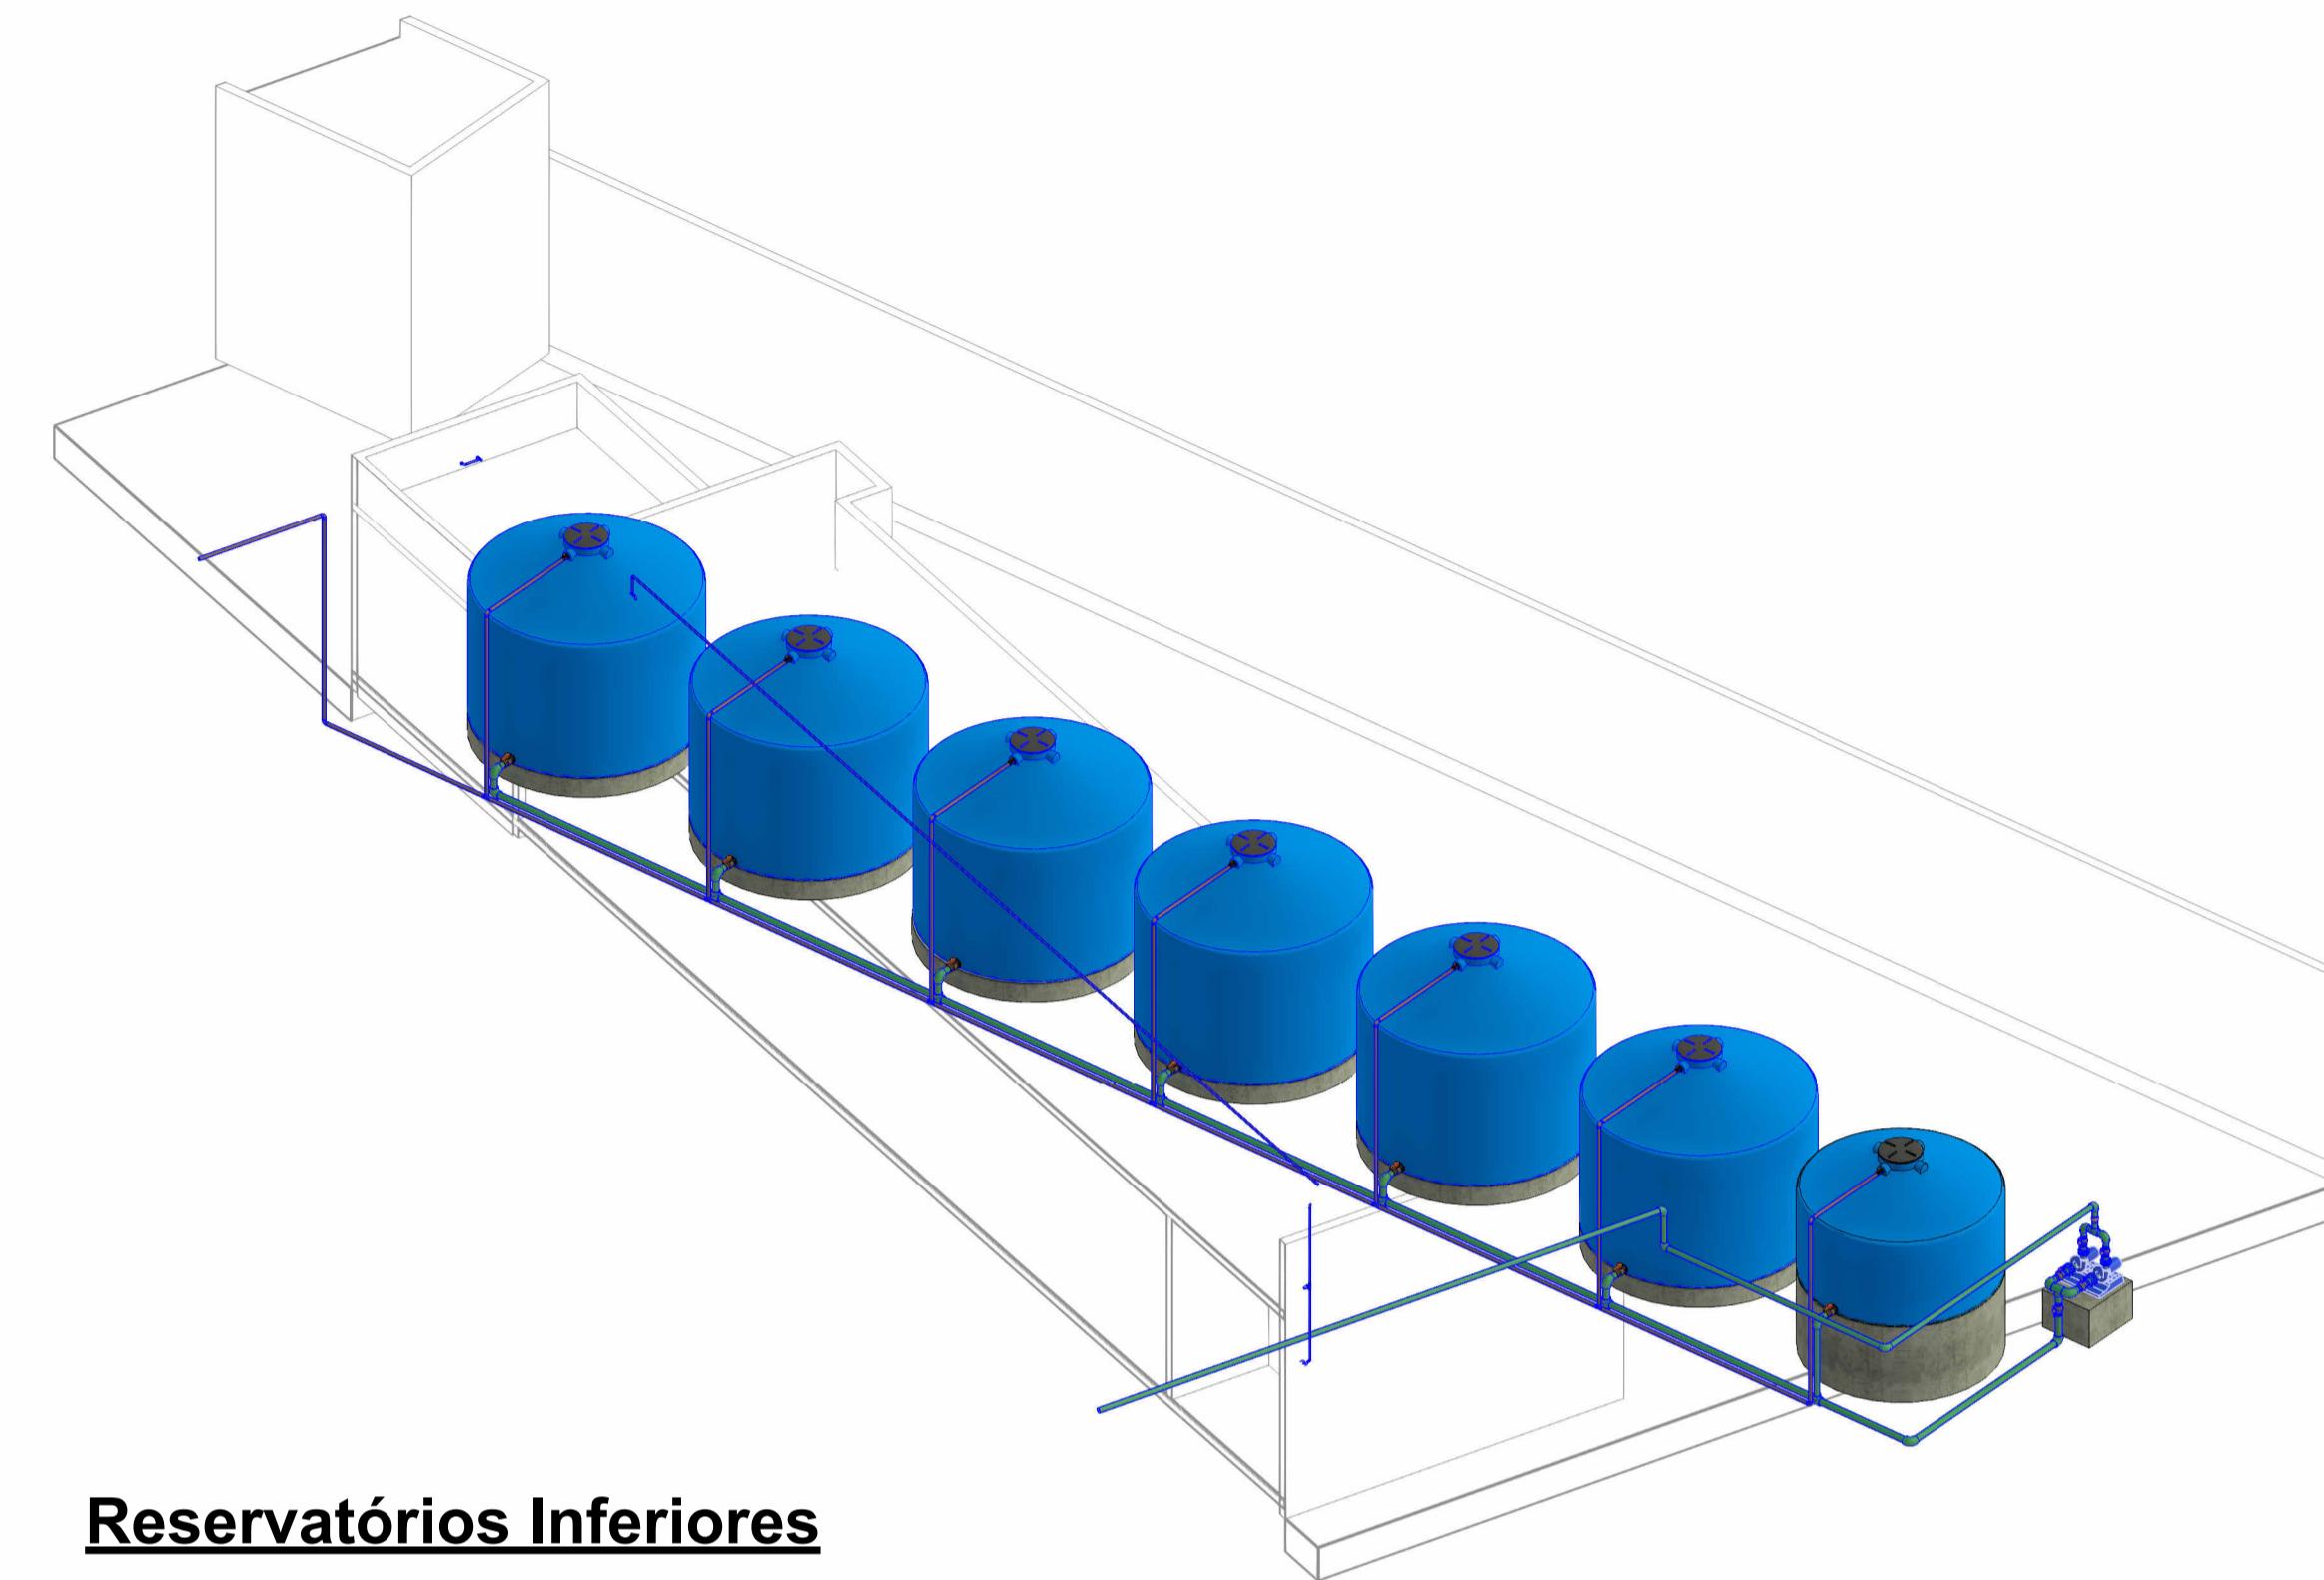


Reservatórios Inferiores

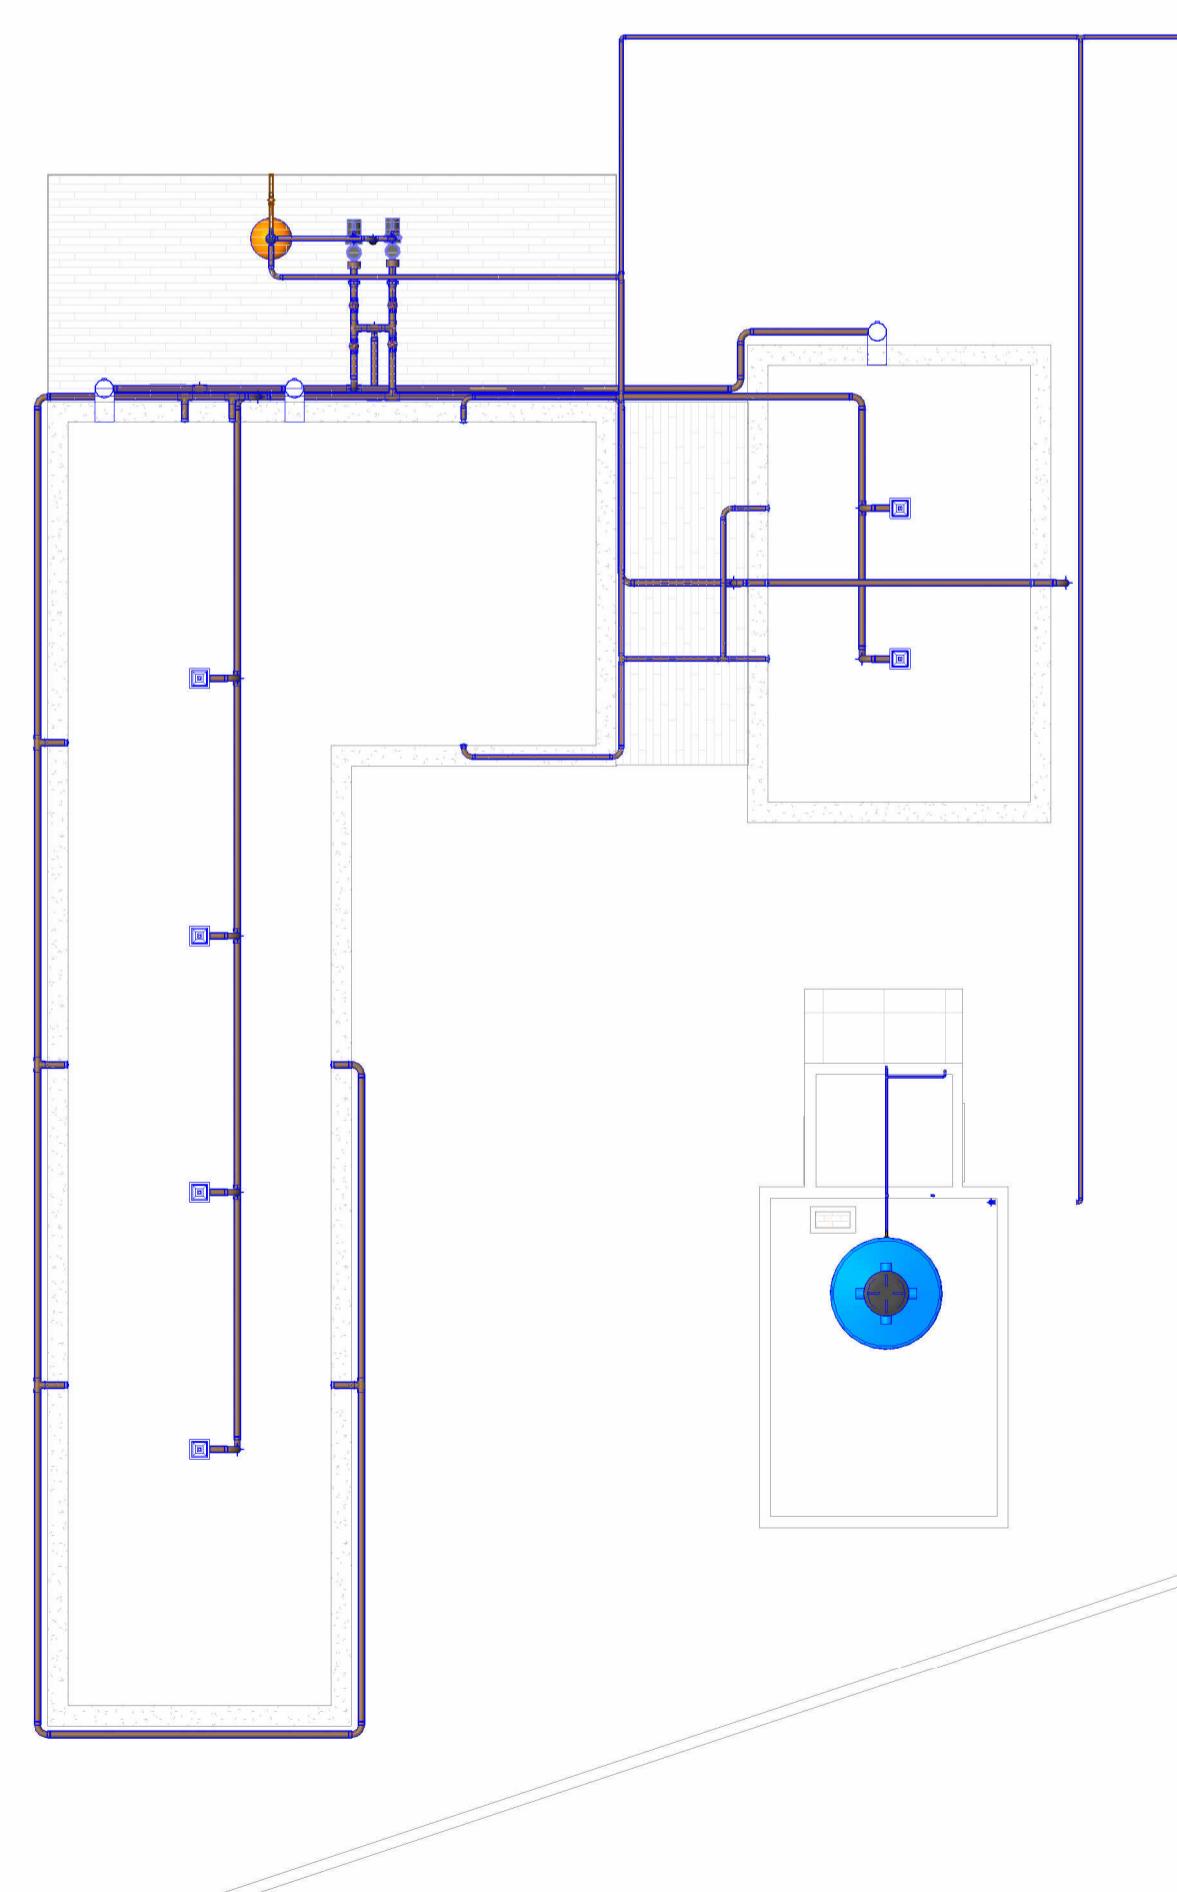

Planta Baixa Piscina

1 : 100

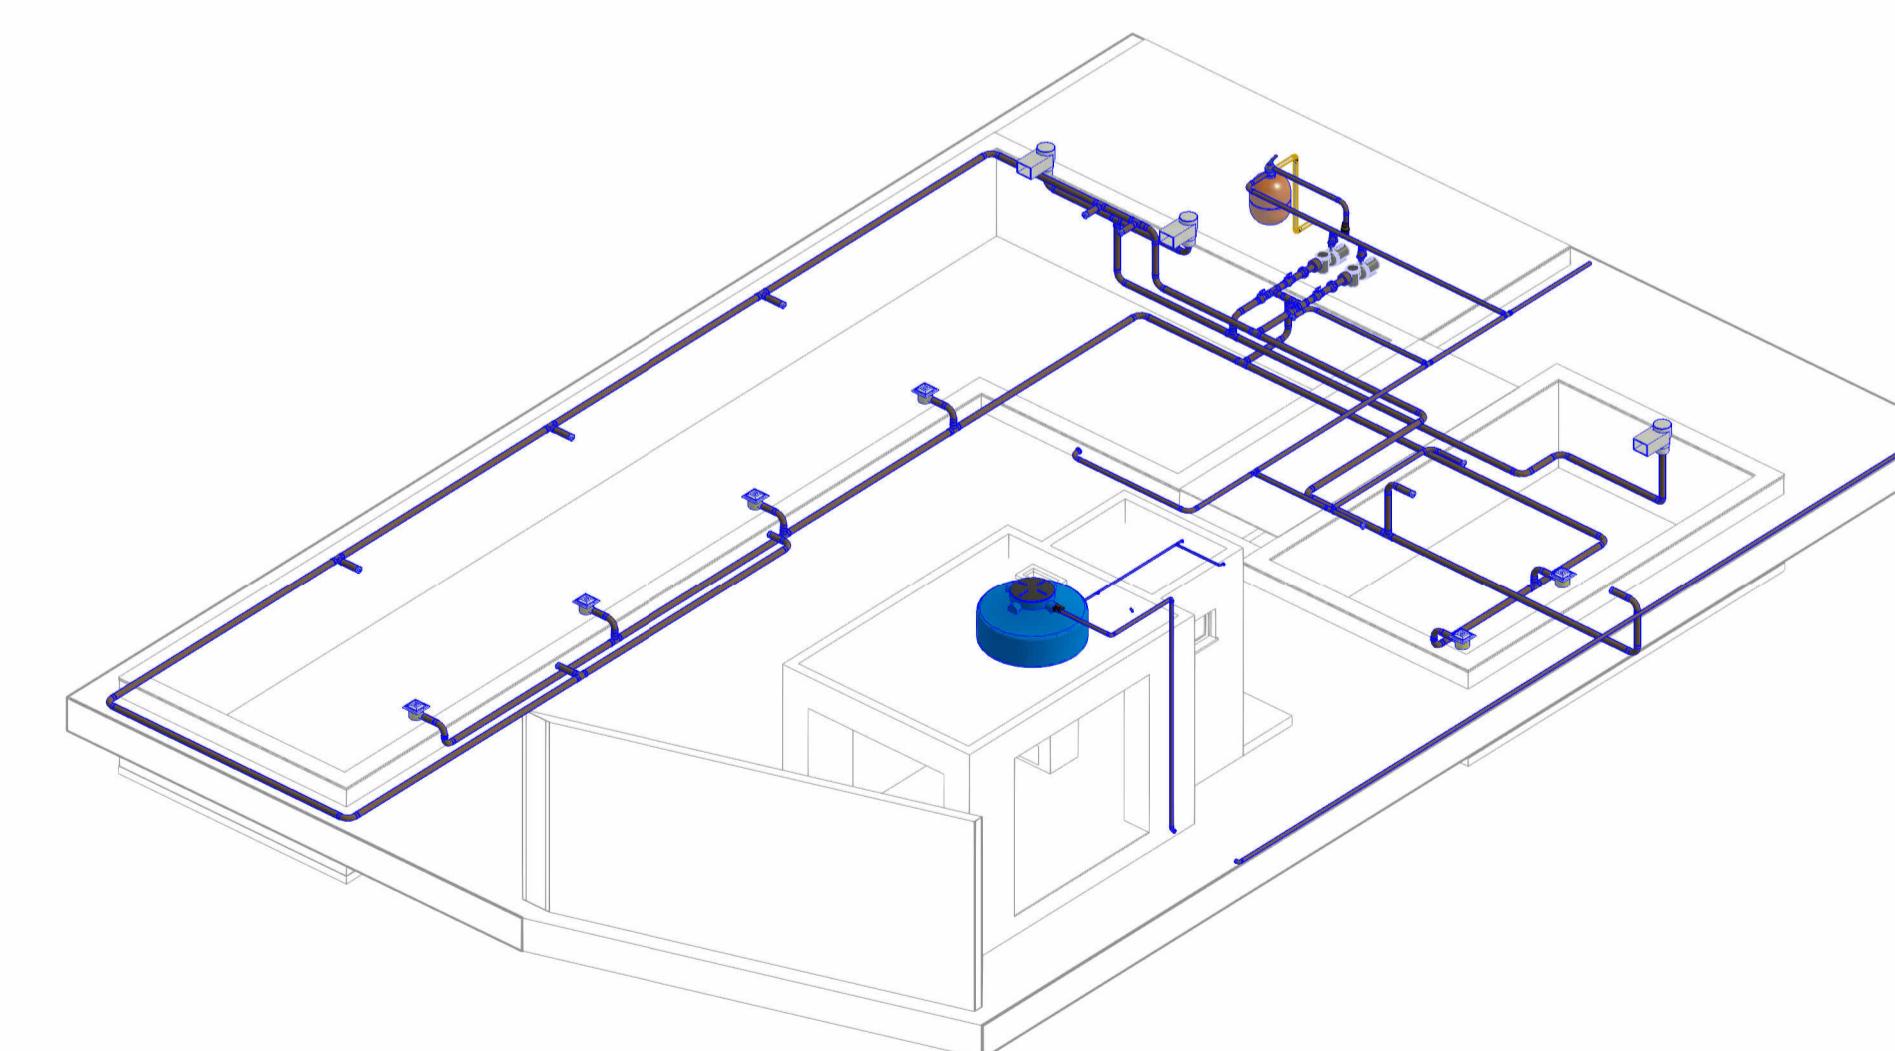


Isométrico Piscina




PENN & WIZE
INSTALAÇÕES PREDIAIS
<https://pennwize.github.io/>


PROJETO:	EDIFÍCIO DERRY AND GEORGIE	FOLHA:	01
LOCAL:	Rua dos bobos, n° 0	REV.:	
ASSUNTO:	INSTALAÇÕES HIDROSSANITÁRIAS	ESCALA:	1 : 100
AUTORES DO PROJETO:	AMANDA C, JOÃO PEDRO M, LETÍCIA T	DATA:	23/01/26

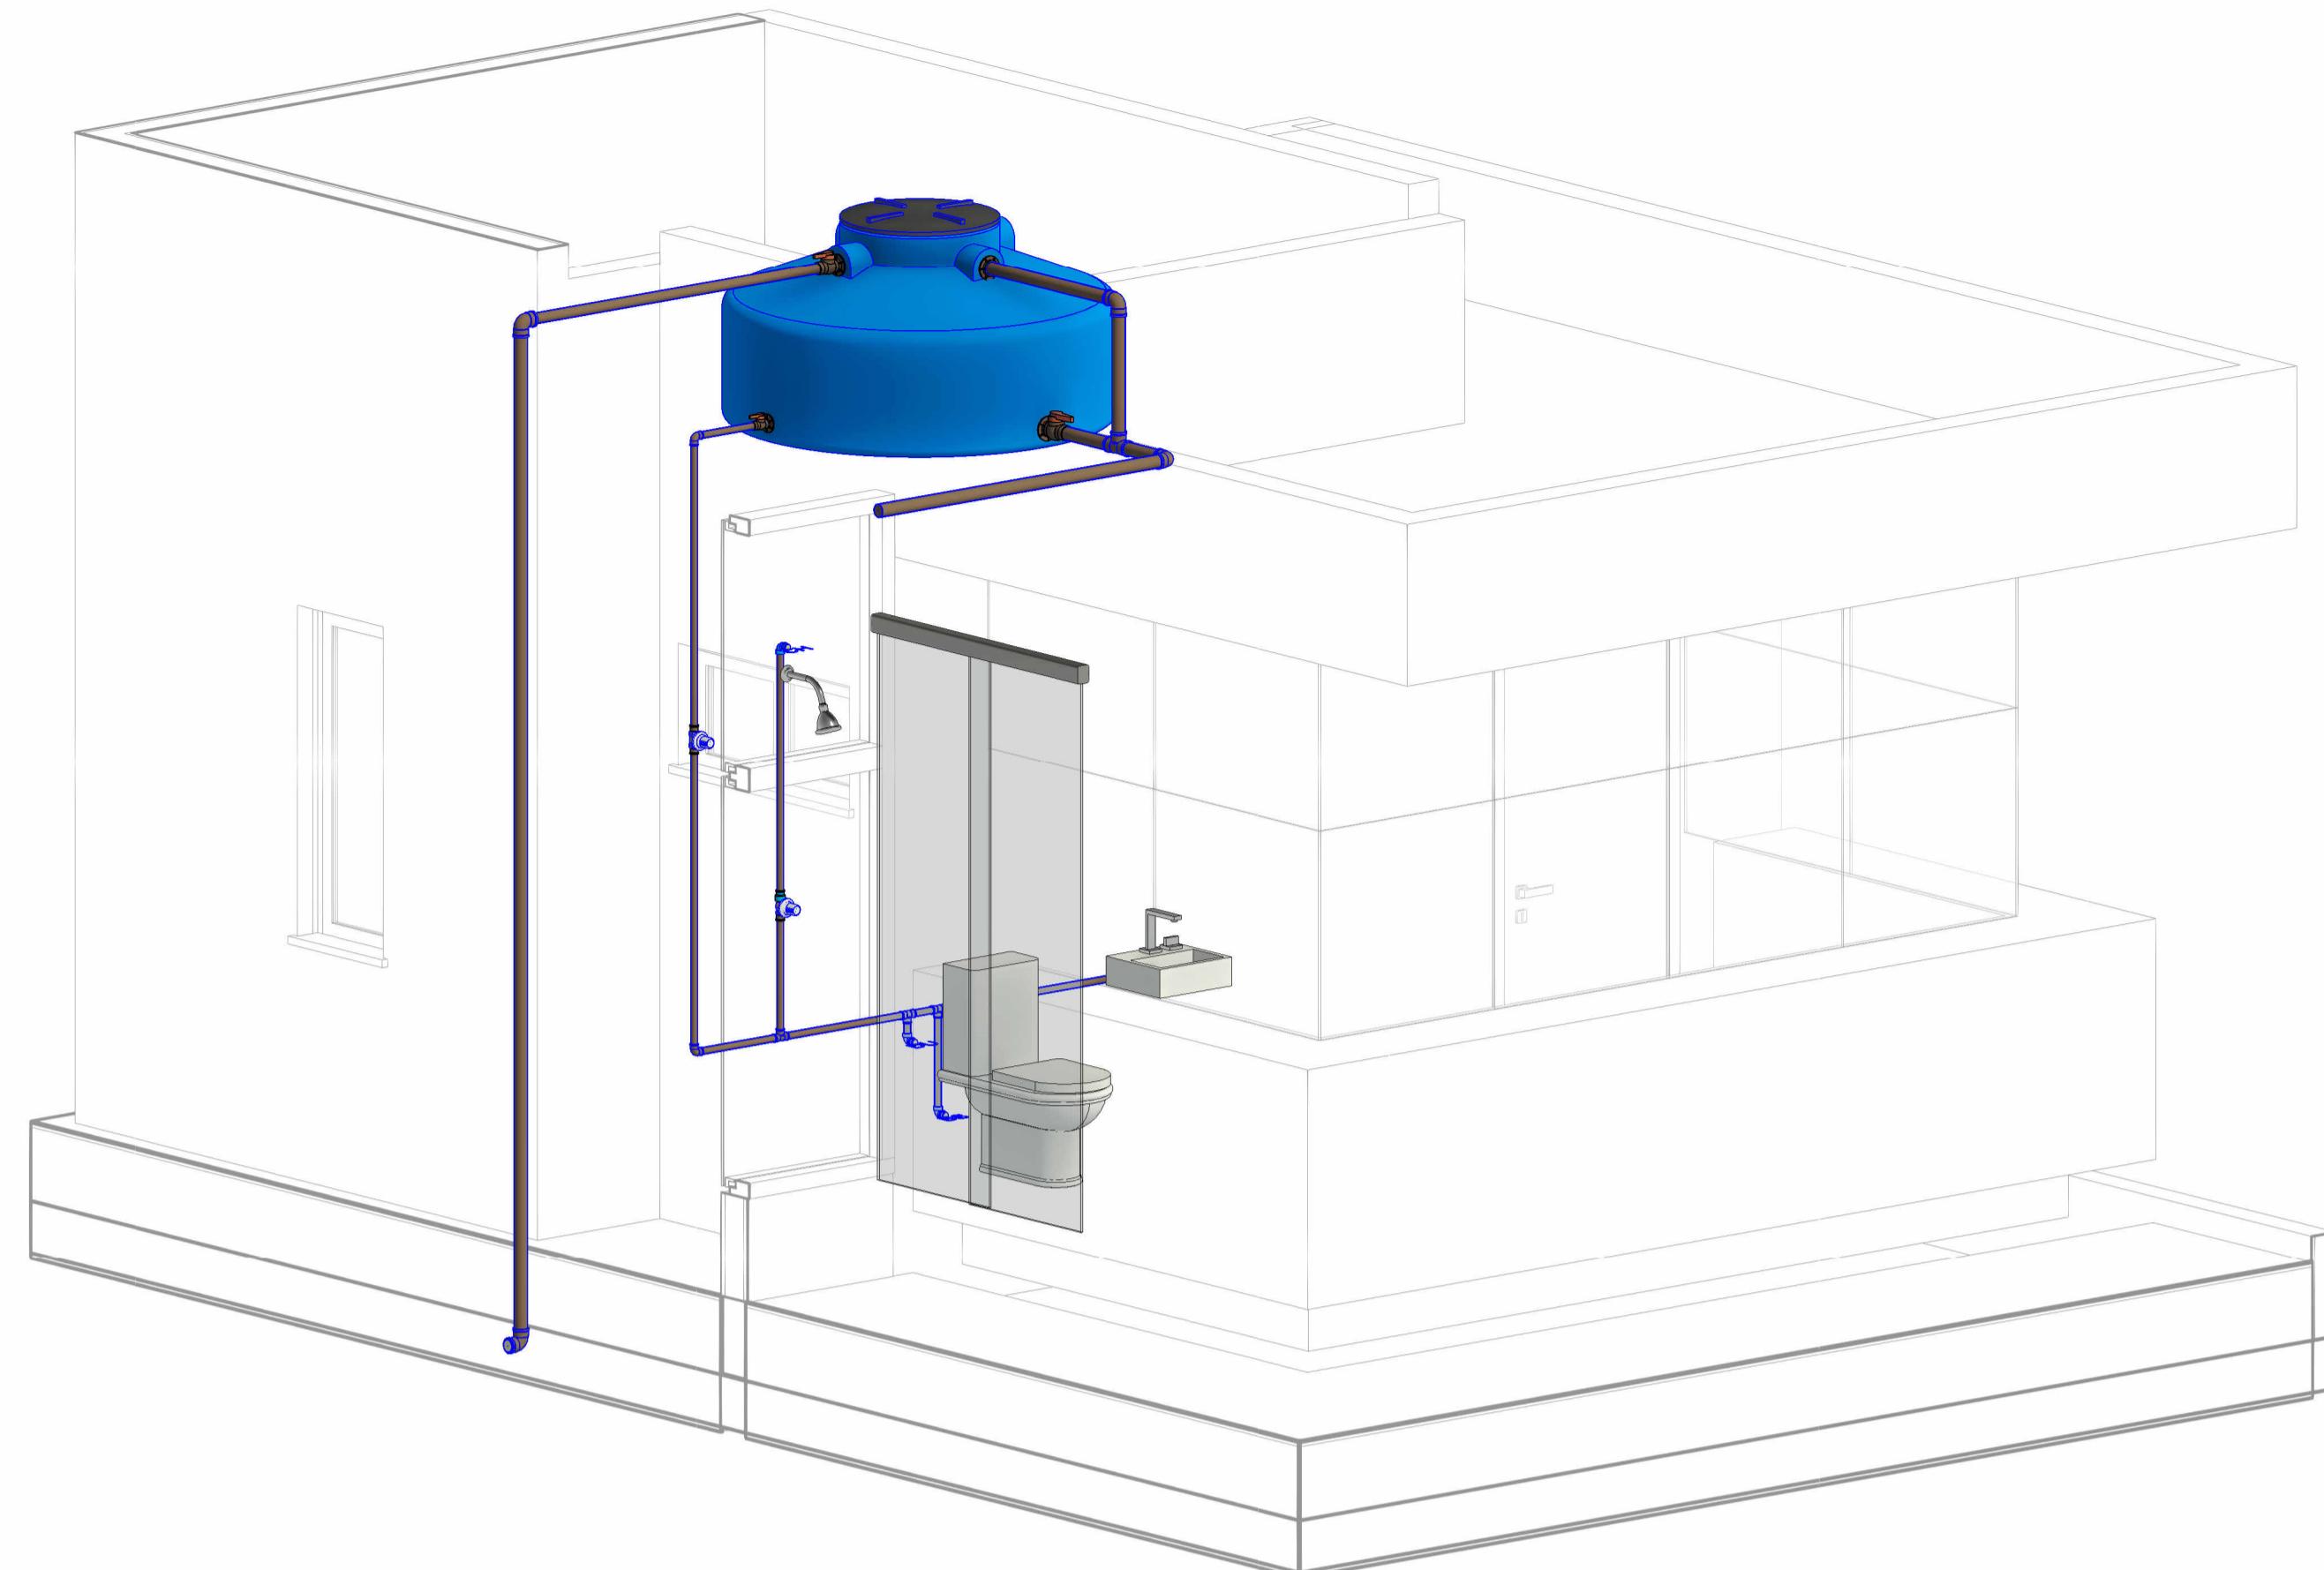


GUARITA

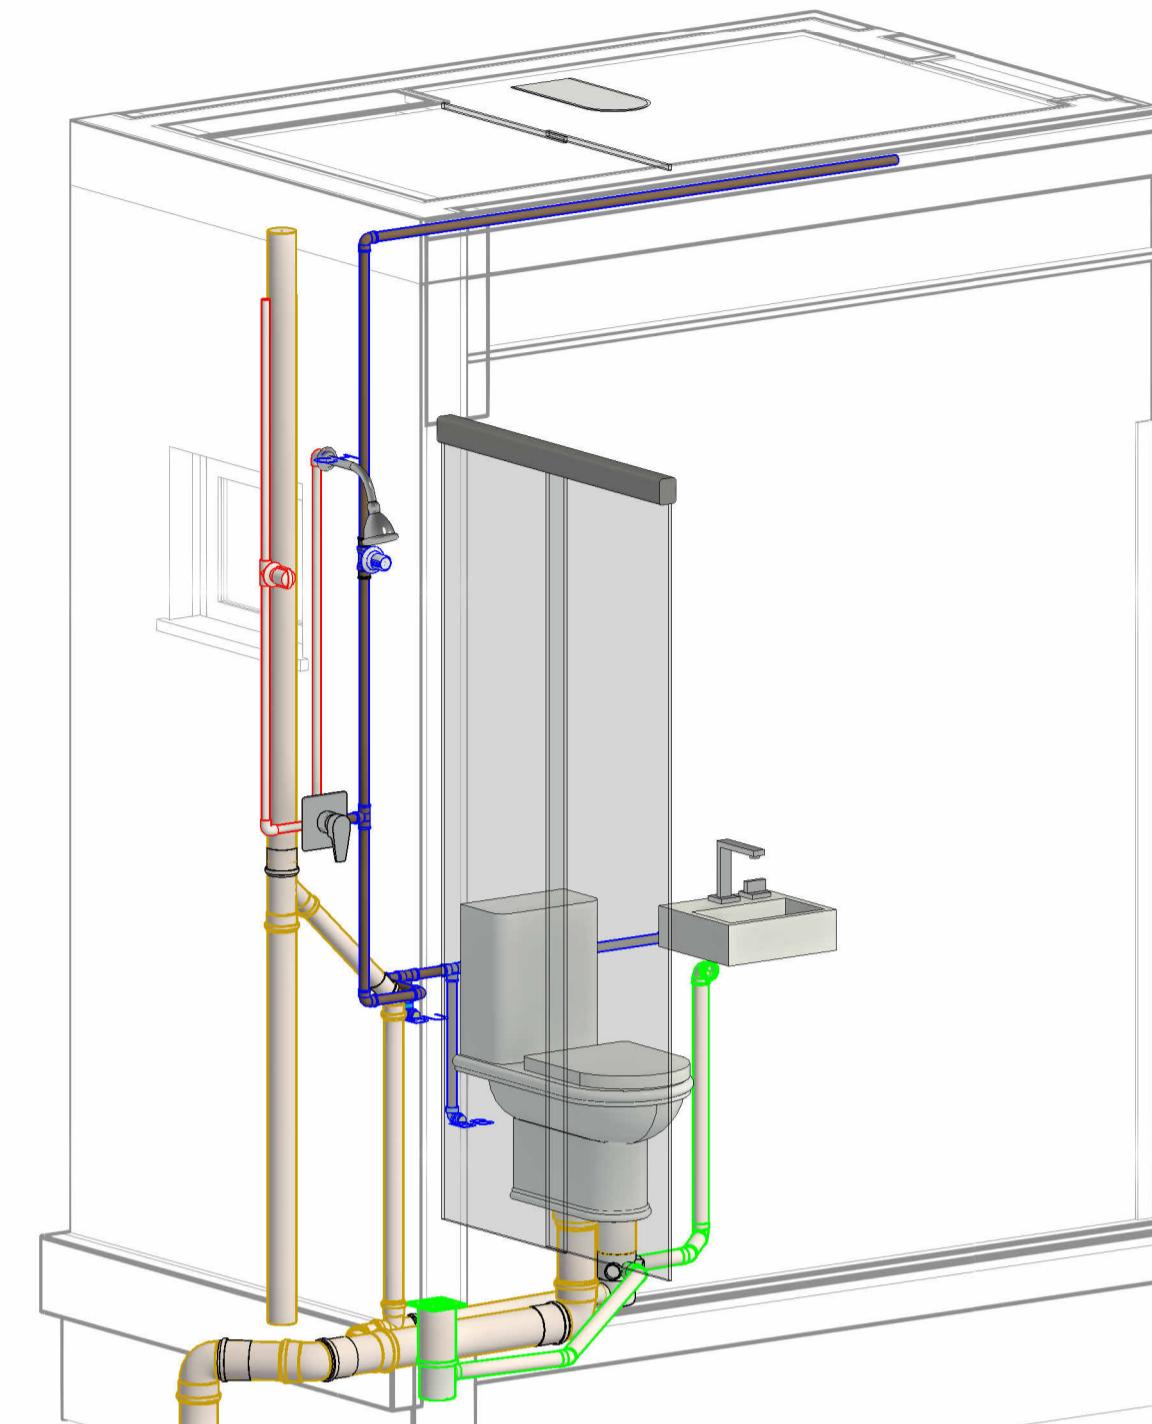

BANHEIRO MODELO 1

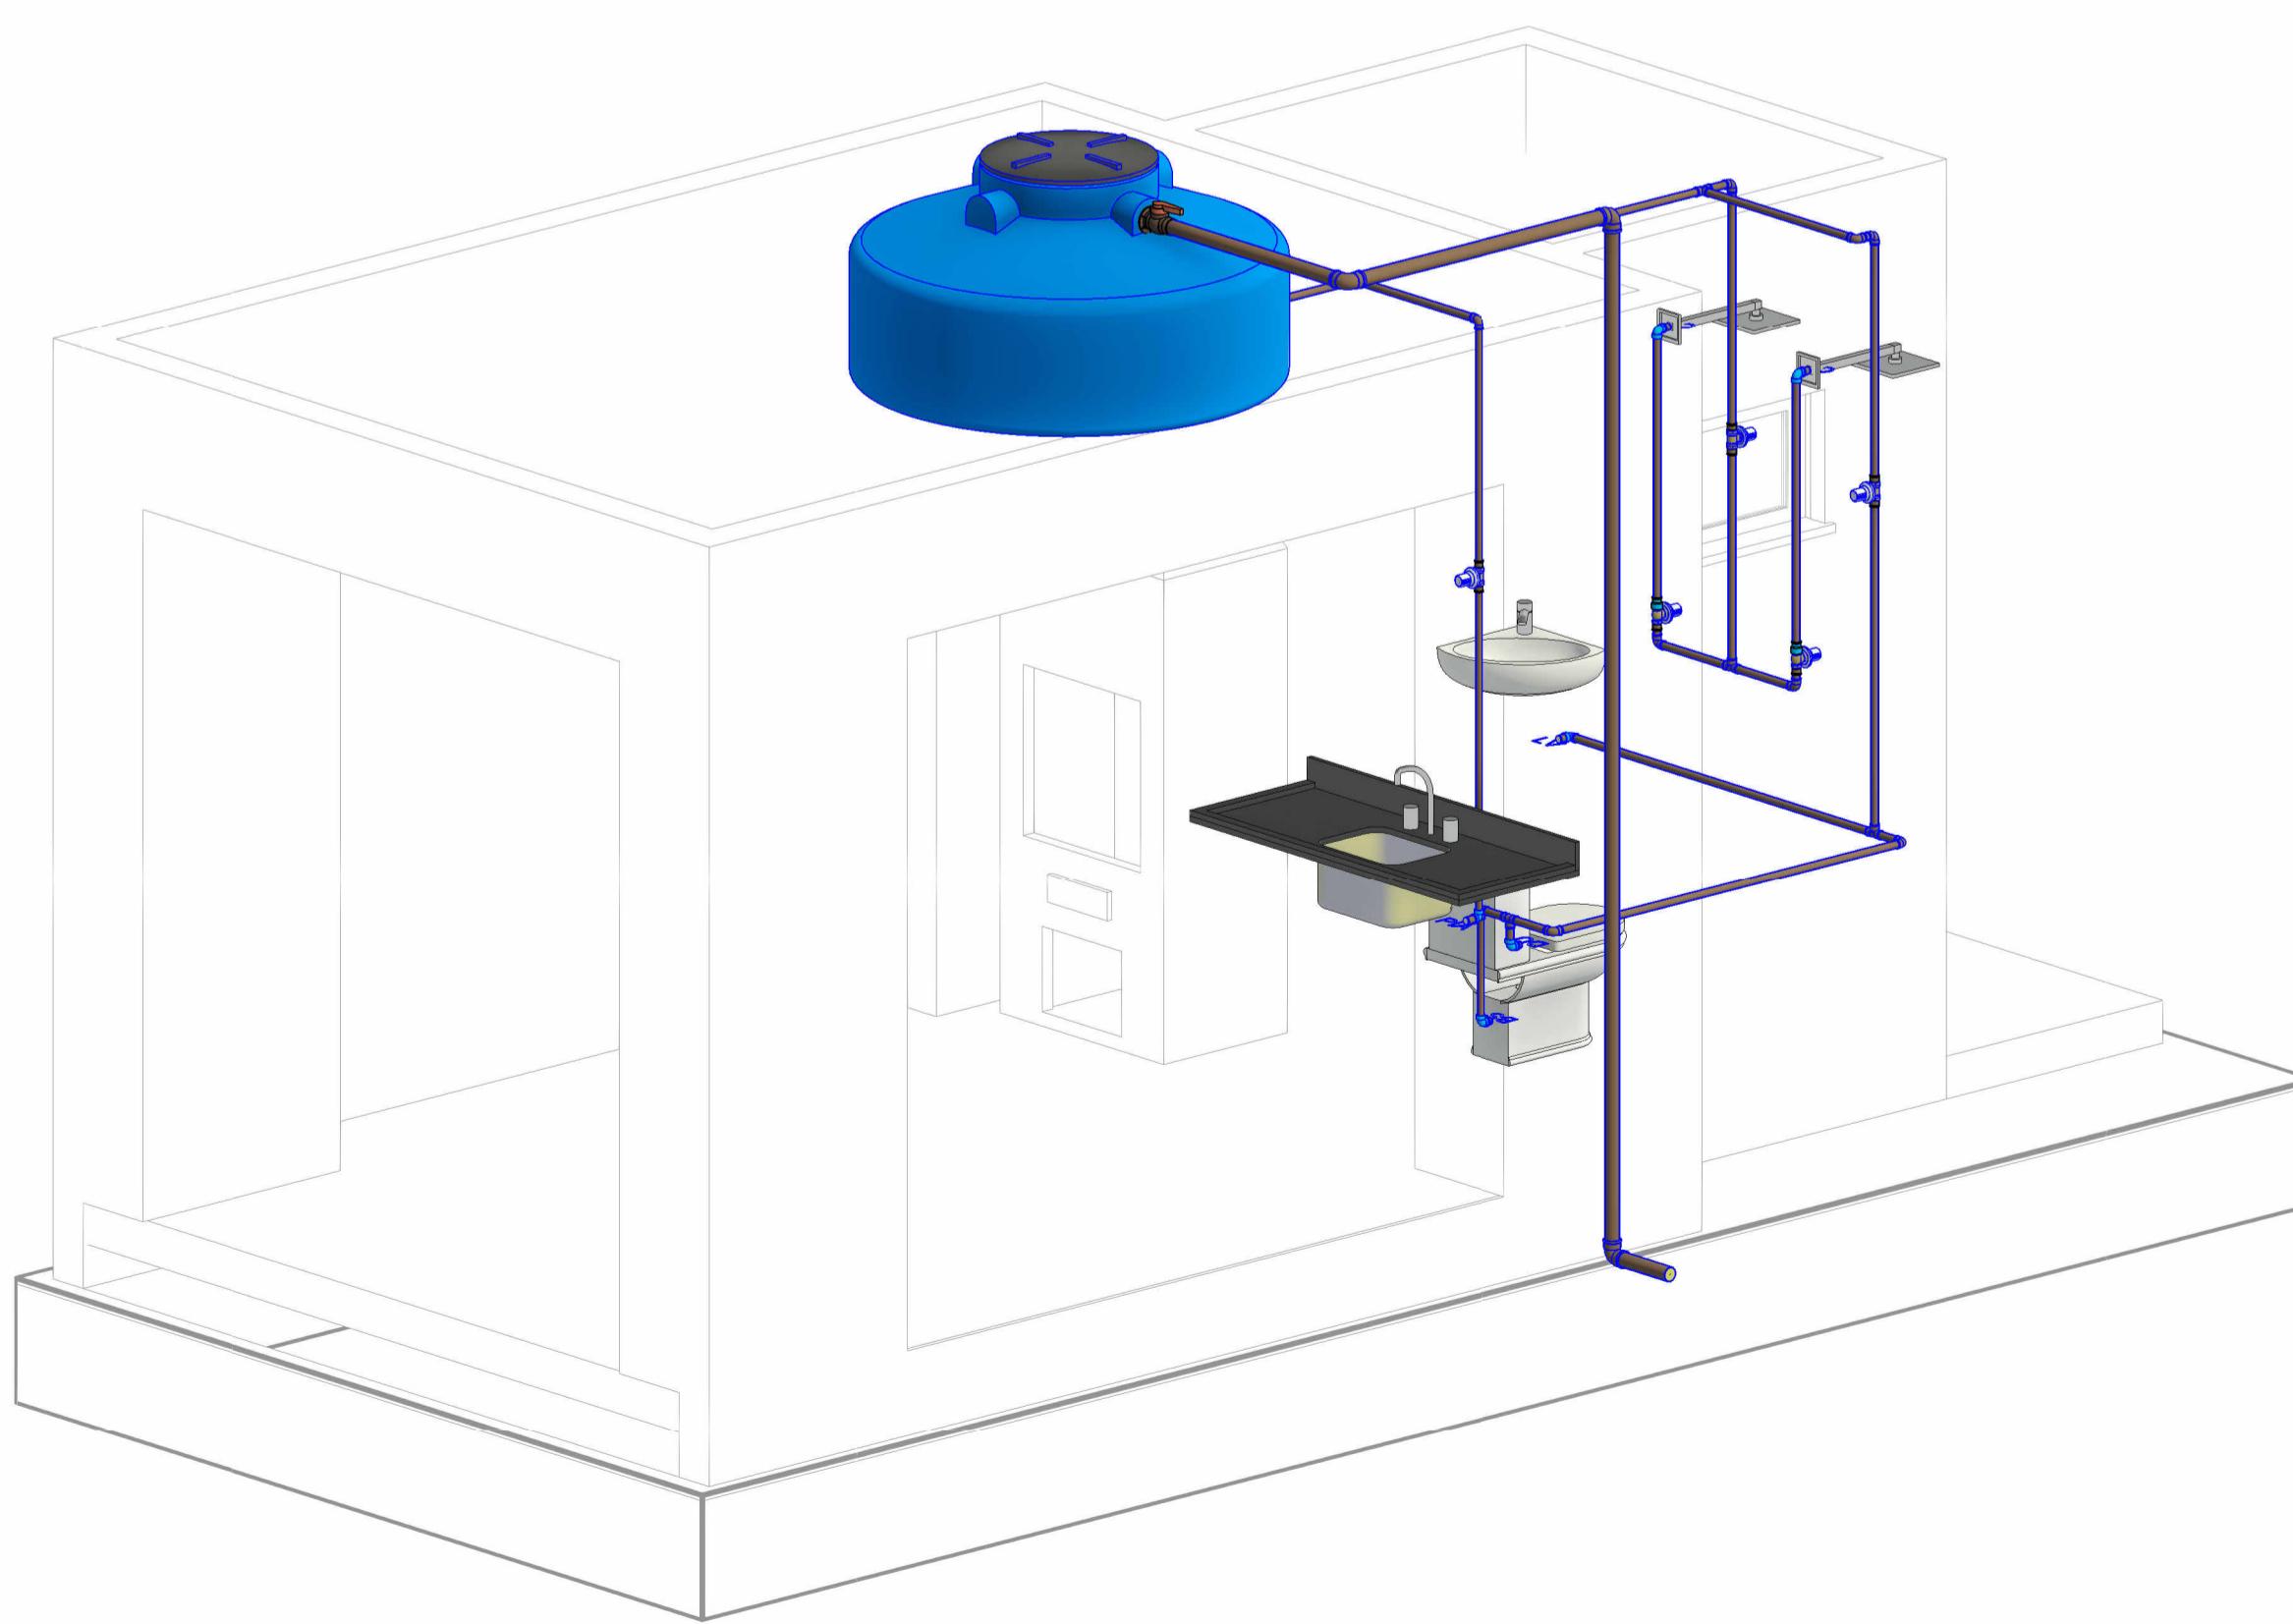

CHURRASQUEIRA

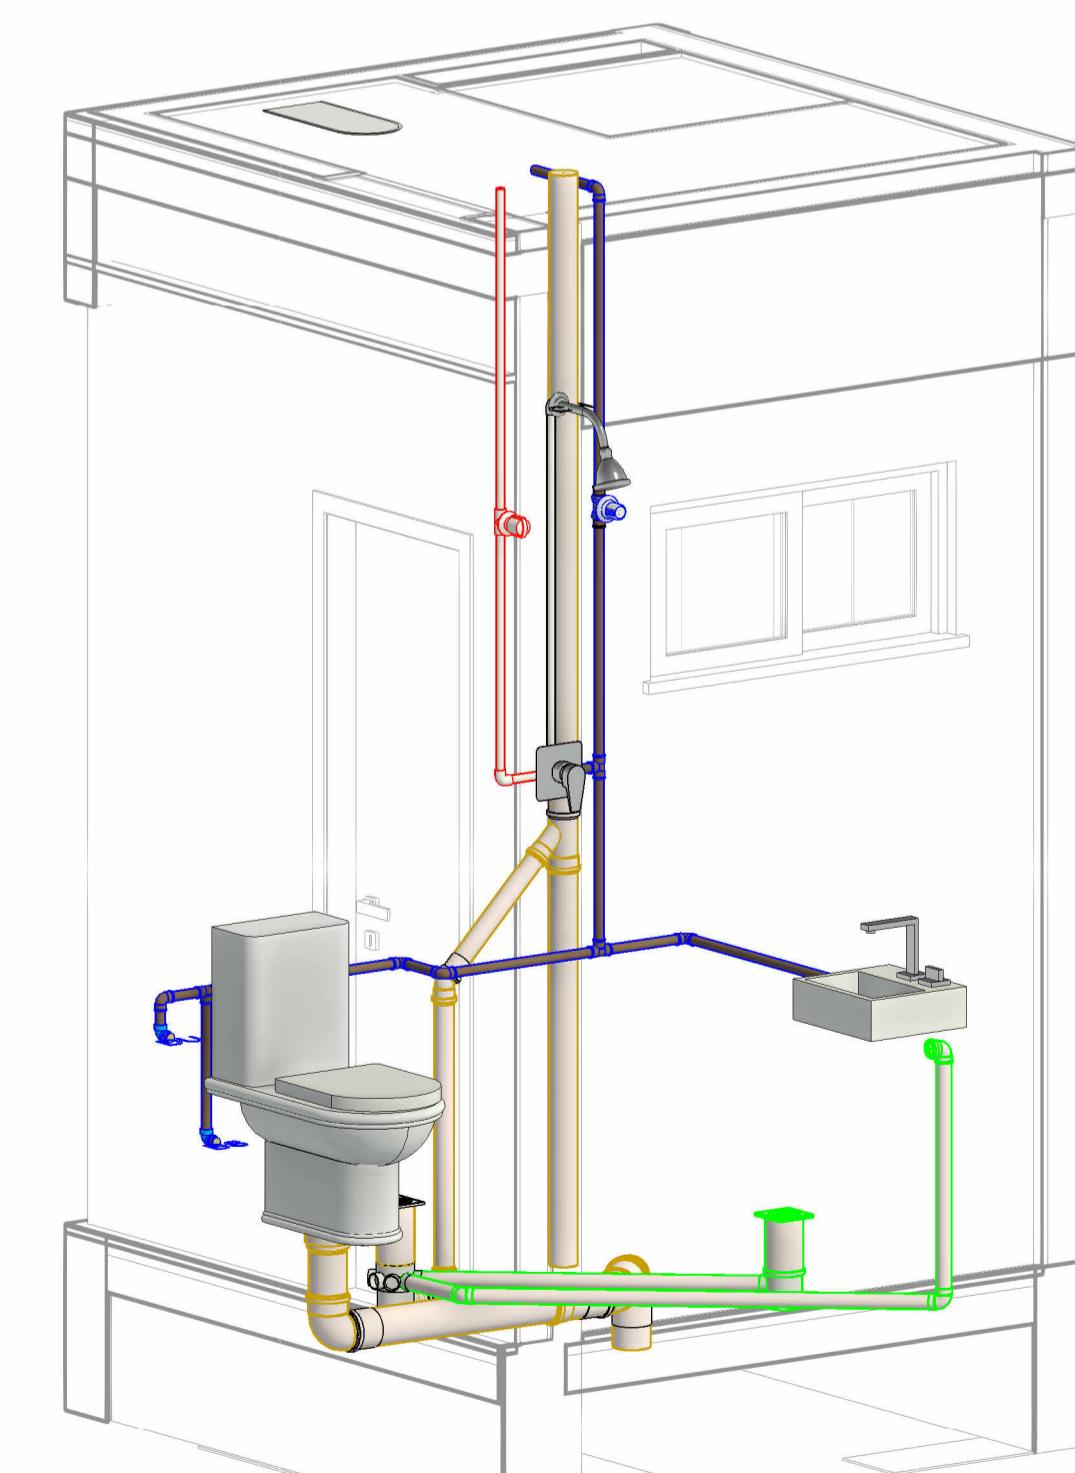


BANHEIRO MODELO 2



PENN & WIZE
INSTALAÇÕES PREDIAIS
<https://pennwize.github.io/>

PROJETO:	EDIFÍCIO DERRY AND GEORGIE	FOLHA:	02
LOCAL:	Rua dos bobos, n° 0	REV.:	
ASSUNTO:	INSTALAÇÕES HIDROSSANITÁRIAS	ESCALA:	
AUTORES DO PROJETO:	AMANDA C, JOÃO PEDRO M, LETÍCIA T	DATA:	23/01/26

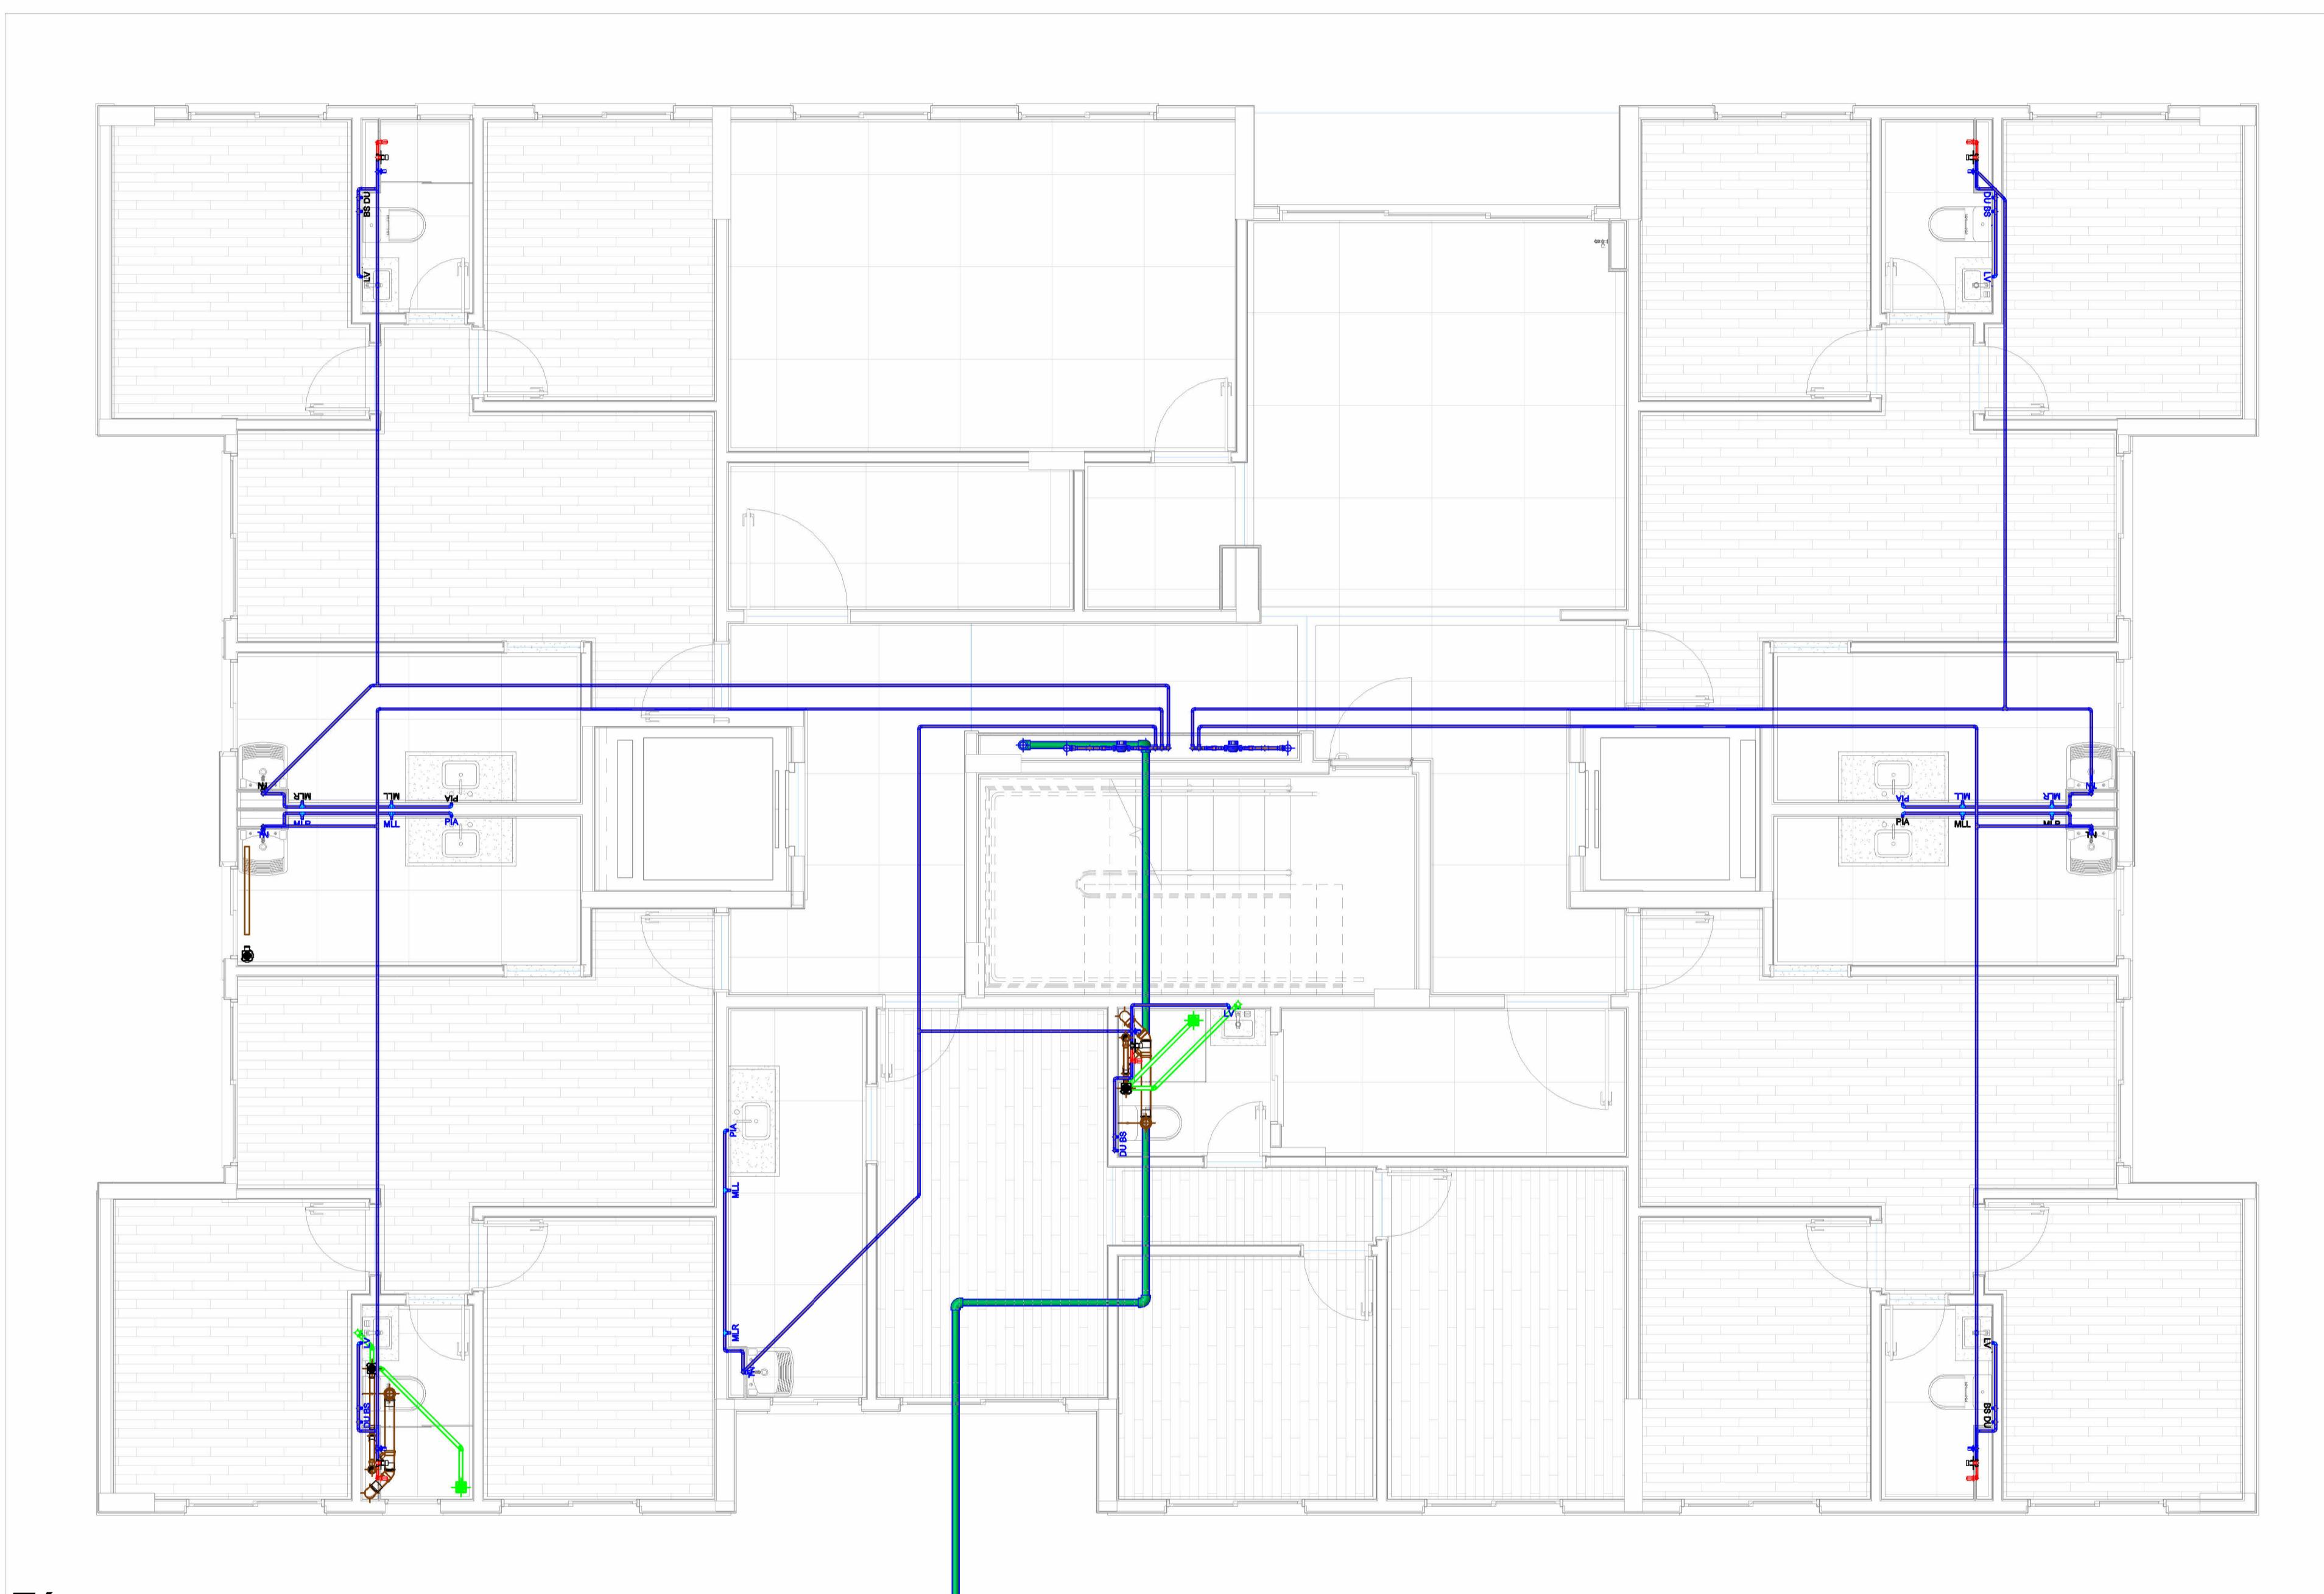


Térreo

1 : 50



PENN & WIZE
INSTALAÇÕES PREDIAIS
<https://pennwize.github.io/>

PROJETO:	EDIFÍCIO DERRY AND GEORGIE	FOLHA:	03
LOCAL:	Rua dos bobos, n° 0	REV.:	
ASSUNTO:	INSTALAÇÕES HIDROSSANITÁRIAS	ESCALA:	1 : 50
AUTORES DO PROJETO:	AMANDA C, JOÃO PEDRO M, LETÍCIA T	DATA:	23/01/26

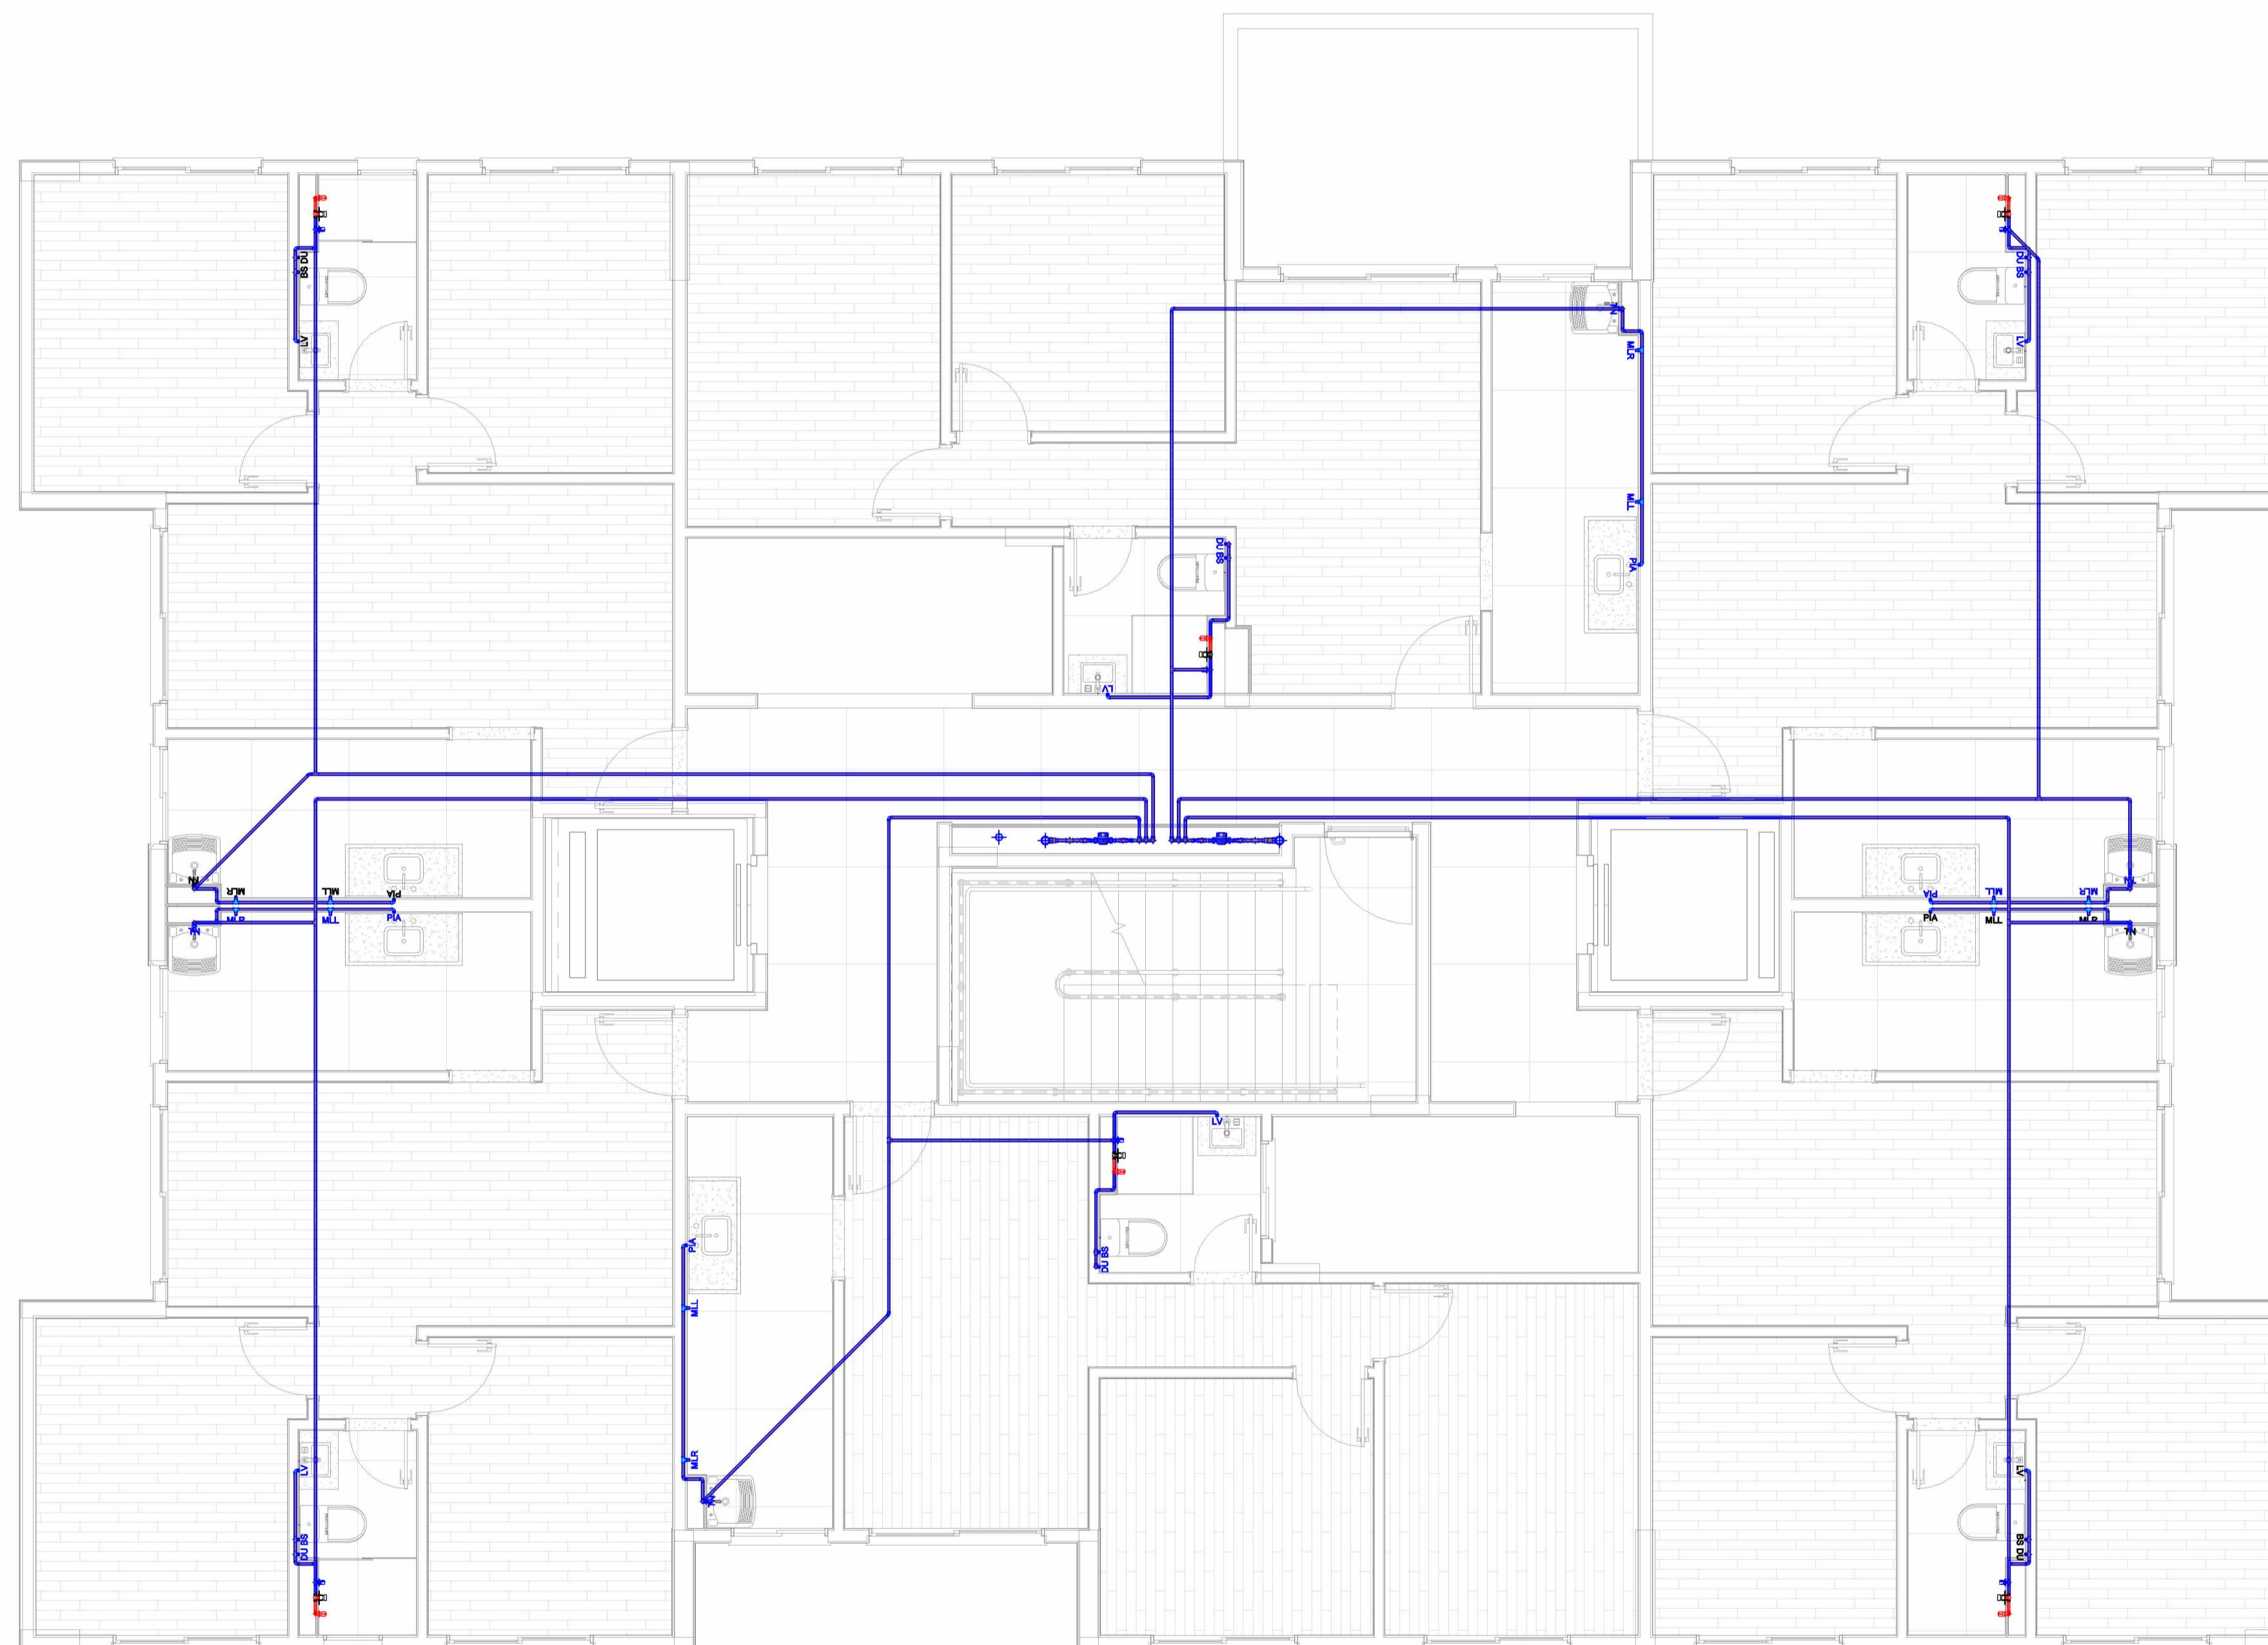

1º Pavimento

1 : 50



PENN & WIZE
INSTALAÇÕES PREDIAIS

<https://pennwize.github.io/>

PROJETO:	EDIFÍCIO DERRY AND GEORGIE	FOLHA:	04
LOCAL:	Rua dos bobos, nº 0	REV.:	
ASSUNTO:	INSTALAÇÕES HIDROSSANITÁRIAS	ESCALA:	1 : 50
AUTORES DO PROJETO:	AMANDA C, JOÃO PEDRO M, LETÍCIA T	DATA:	23/01/26